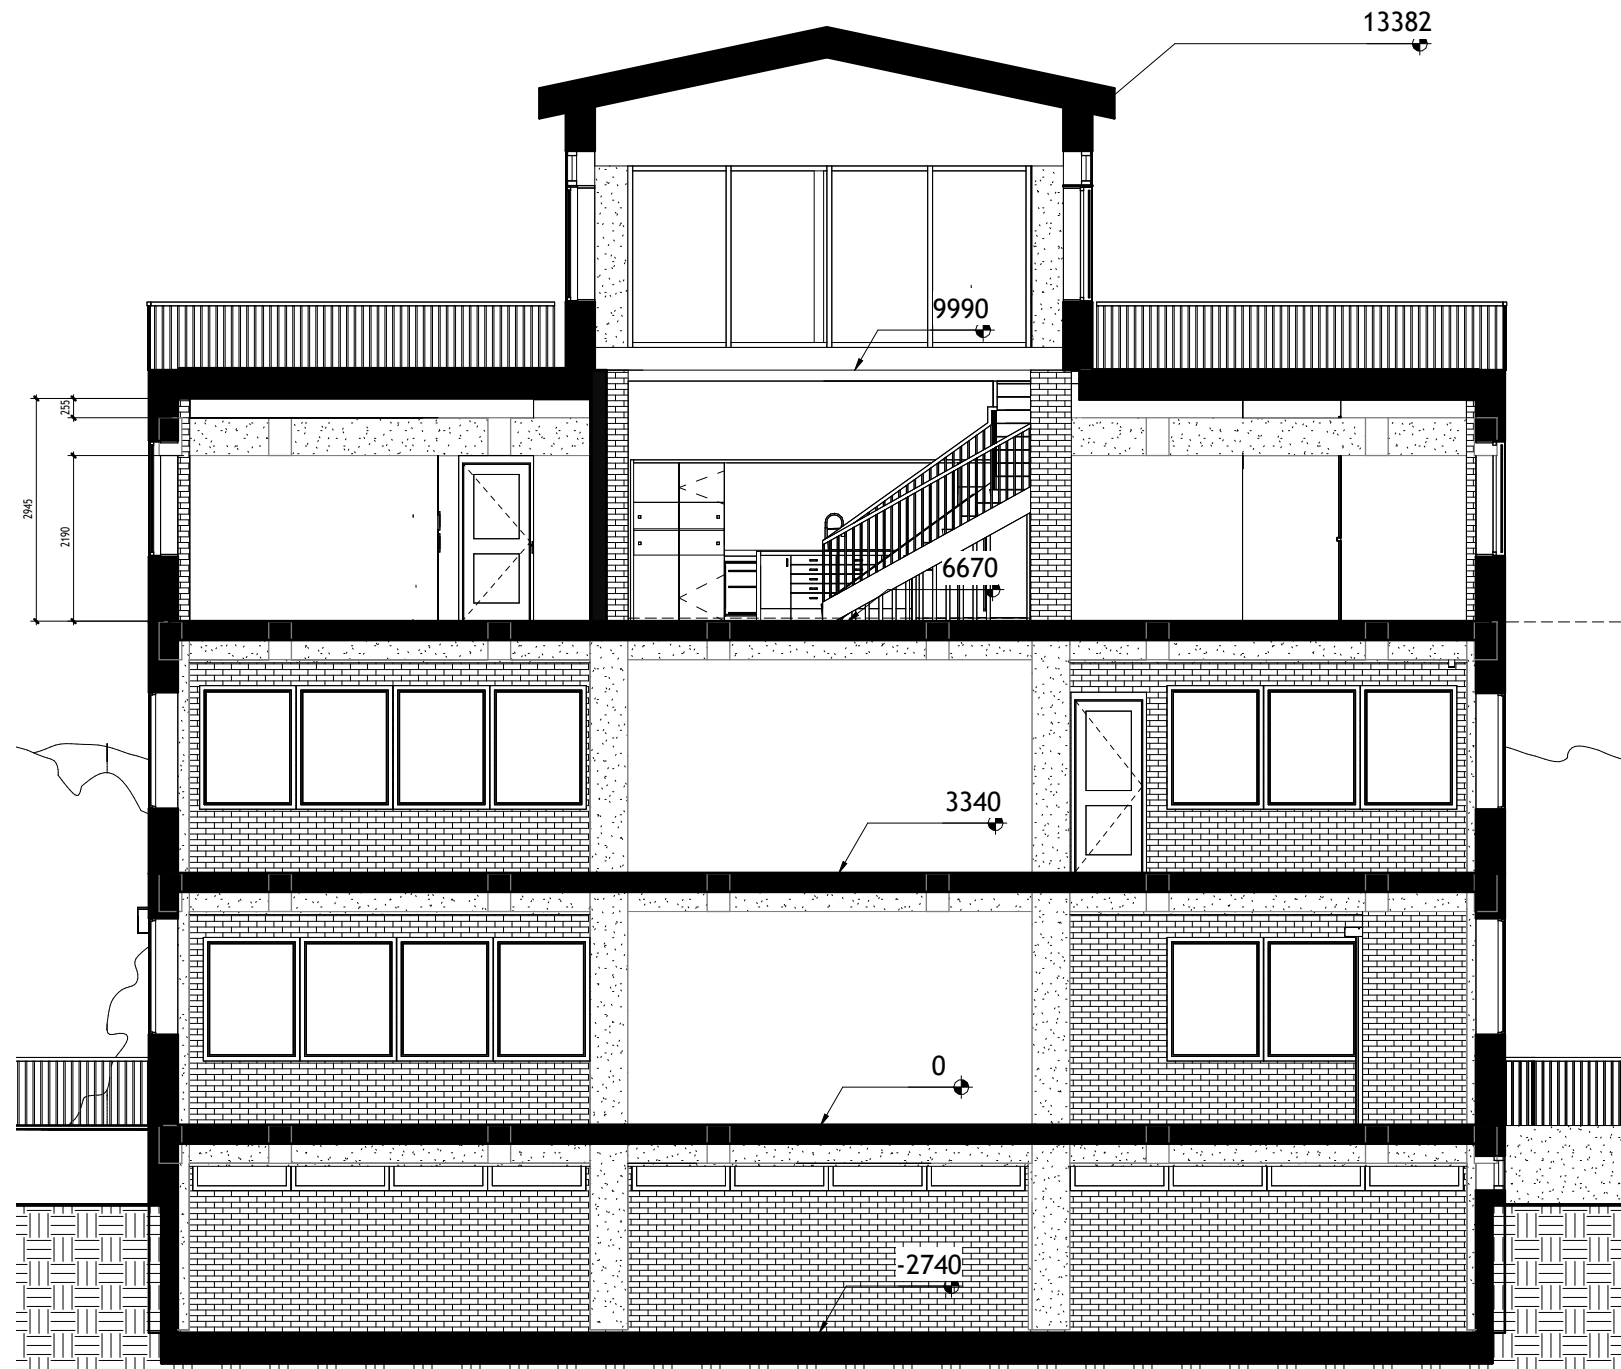


BET	ANT	ÄNDRINGEN AVSER	DATUM	SIGN
Systemhandling				
LÖVHOLMEN 12				
UPPDRAG NR		RTAD/KONSTR. AV	HANDLAGGARE	
		F.F		
DATUM		ANSVARIG		
12/11/25		M.B. , F.F		
Sektion B-B				
SKALA		NUMMER		BET
A1	As indicated	A-40-2-2		A
A3	1: 100			